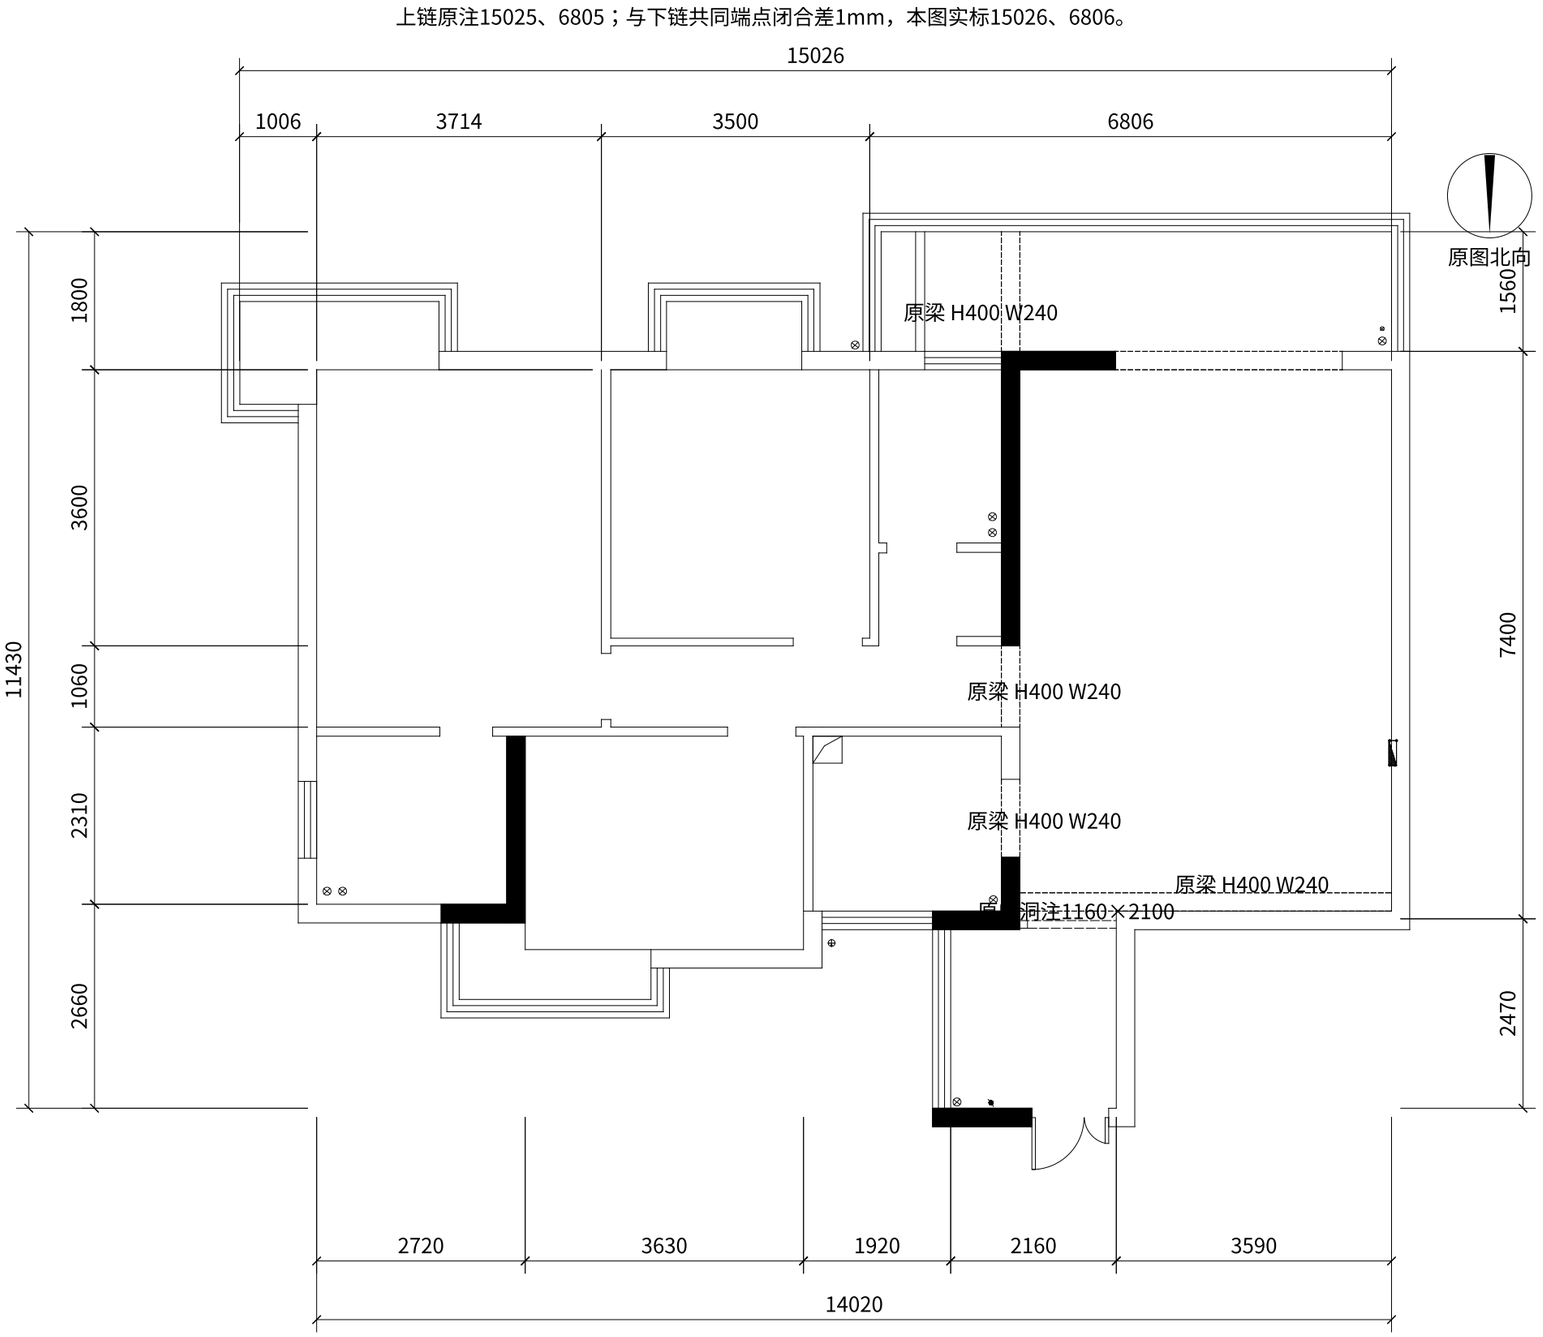


原始结构校核图 1:80

盛苑新街 5栋901

原始结构校核图

夫妻二人 / 现代轻法式 / 独立书房

底图与尺寸依据


01 底图来自客户提供的矢量PDF。
02 外轮廓、梁、门窗及承重墙柱原位保留。
03 原始DWG保留原文件，未直接转换或改写。
04 坐标按原尺寸链分段校准，模型单位mm。
05 上链与下链同端闭合差1mm，待实测确认。
06 顶部原注15025；模型闭合15026。
07 右上原注6805；模型闭合6806。
08 其它已选尺寸链按原图闭合。
09 层高2800；卫生间下沉400。
10 多处原梁高400、宽240。
11 1160×2100为玄关上端门洞注记。
12 下端双扇入户门按源图保留。
13 原图未注明每个房间用途。
14 厨卫定位结合原燃气/排水点推定。
15 现场需复测窗台、梁底及管道口。
16 北针方向沿用原图，不据图面上下命名。

平面方案 R1 · 待业主及现场复核

A01　A3　1:80　单位:mm

2026-11-04

上链原注15025、6805；与下链共同端点闭合差1mm，本图实标15026、6806。

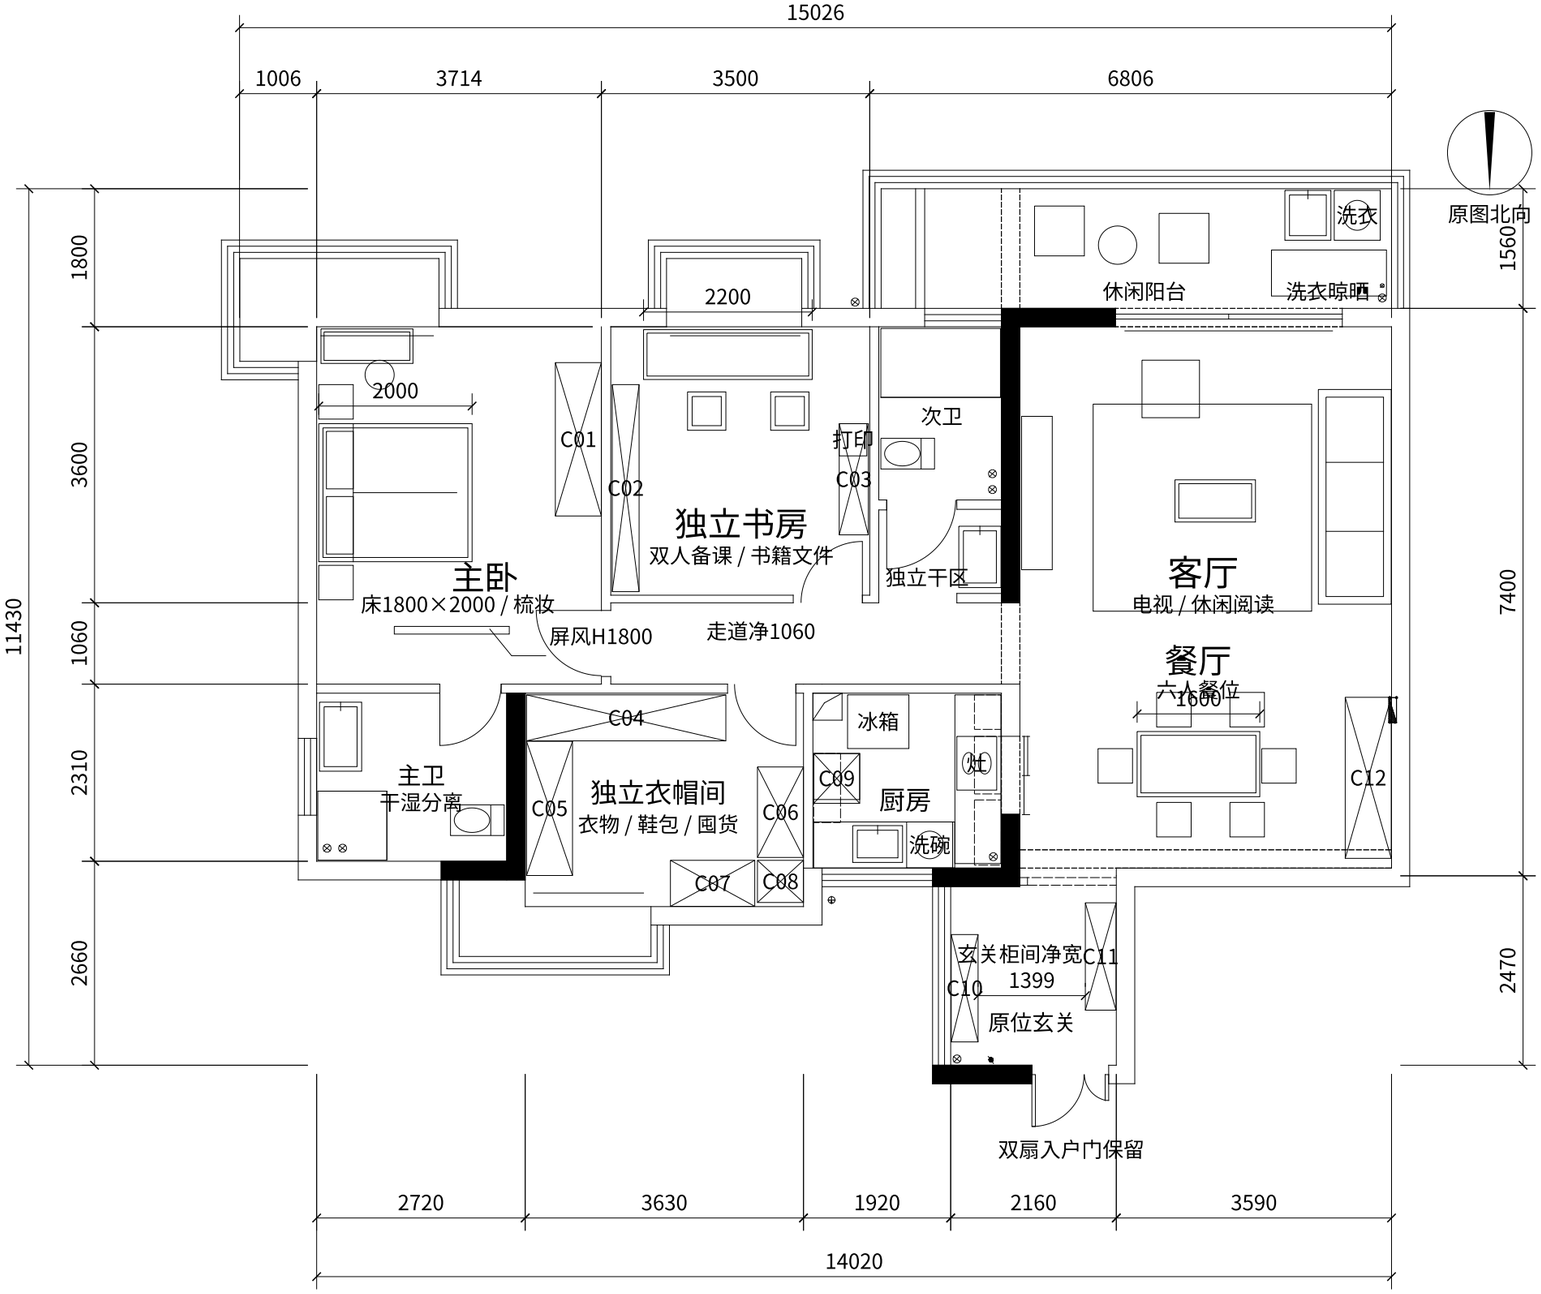

家具平面布置图 1:80

盛苑新街 5栋901

家具平面布置图

夫妻二人 / 现代轻法式 / 独立书房


设计与布置说明

01 主卧+独立书房+独立衣帽储物间。
02 无儿童房，不新增固定客卧。
03 主卧1800×2000床，1200梳妆台。
04 主卫门外1500屏风遮挡床视线。
05 书房2200双人桌，教师备课及打印。
06 主卧、书房原飘窗均保留。
07 衣帽间设分类柜，飘窗前留空。
08 厨房限定在原下部独立房间内。
09 窗下洗涤，右侧灶台，原侧门保留。
10 厨房冰箱/洗碗机/消毒柜均有位置。
11 玄关及入户门不移动、不扩轮廓。
12 玄关窗下鞋柜H≤900，避免遮窗。
13 右侧客餐厅，六人餐桌1600×850。
14 上部阳台右端洗衣晾晒，左部休闲。
15 阳台暂以软分区分开，不另封外墙。
16 两卫智能马桶、湿区及镜柜见A03。
17 主卫局部非承重门洞建议扩至800。
18 墙体性质确认后方可实施拆改。

平面方案 R1 · 待业主及现场复核

A02　A3　1:80　单位:mm

2026-11-04

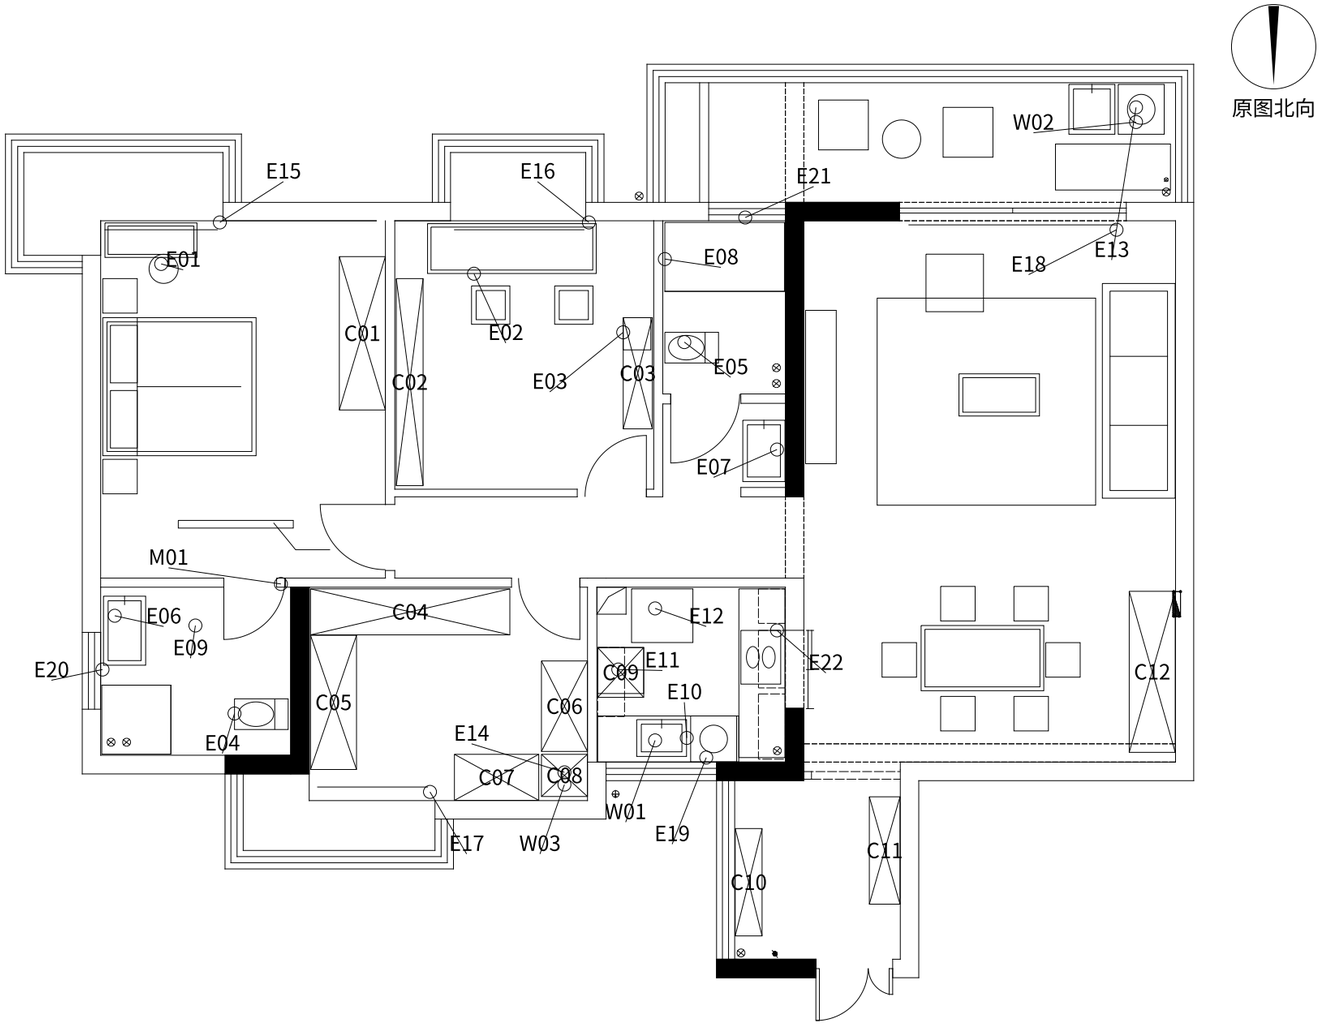

给排水/电气复核：基站设防漏托盘与可检修管路；排水坡度、通气及燃气连接须专业核验。

收纳设备及预留条件图 1:80

盛苑新街 5栋901

收纳设备及预留条件图

夫妻二人 / 现代轻法式 / 独立书房

柜体与设备索引

C01 主卧：600深×2000日常衣柜。
C02 书房：350深×2700封闭书柜。
C03 书房：380深×1450文件/打印柜。
C04 衣帽间：2600×600顶天挂衣柜。
C05 衣帽间：1750×600鞋包/抽屉柜。
C06 衣帽间：1180×600换季/行李柜。
C07 衣帽间：1100×600分类储物柜。
C08 衣帽间：600宽家政基站柜。
C09 厨房：600宽消毒柜/吊柜。
C10 玄关：350深×1400低鞋柜。
C11 玄关：400深×1400储物柜。
C12 餐厅：600深×2100餐边酒柜。
厨房柜/吊柜以电器实物复尺分隔。
浴室镜带化妆灯；两卫三合一浴霸。
厨卫集成吊顶，检修口避开设备。
净水、处理器位于水槽柜下。
W01厨房；W02洗衣；W03扫地基站。
E15—E21全屋电动帘/防潮卷帘预留。
M01 主卫门洞建议800，仅拆约111墙肢。
先核实非承重，不可擅拆。
本图为条件示意，不是施工机电定位图。

平面方案 R1 · 待业主及现场复核

A03　A3　1:80　单位:mm

2026-11-04